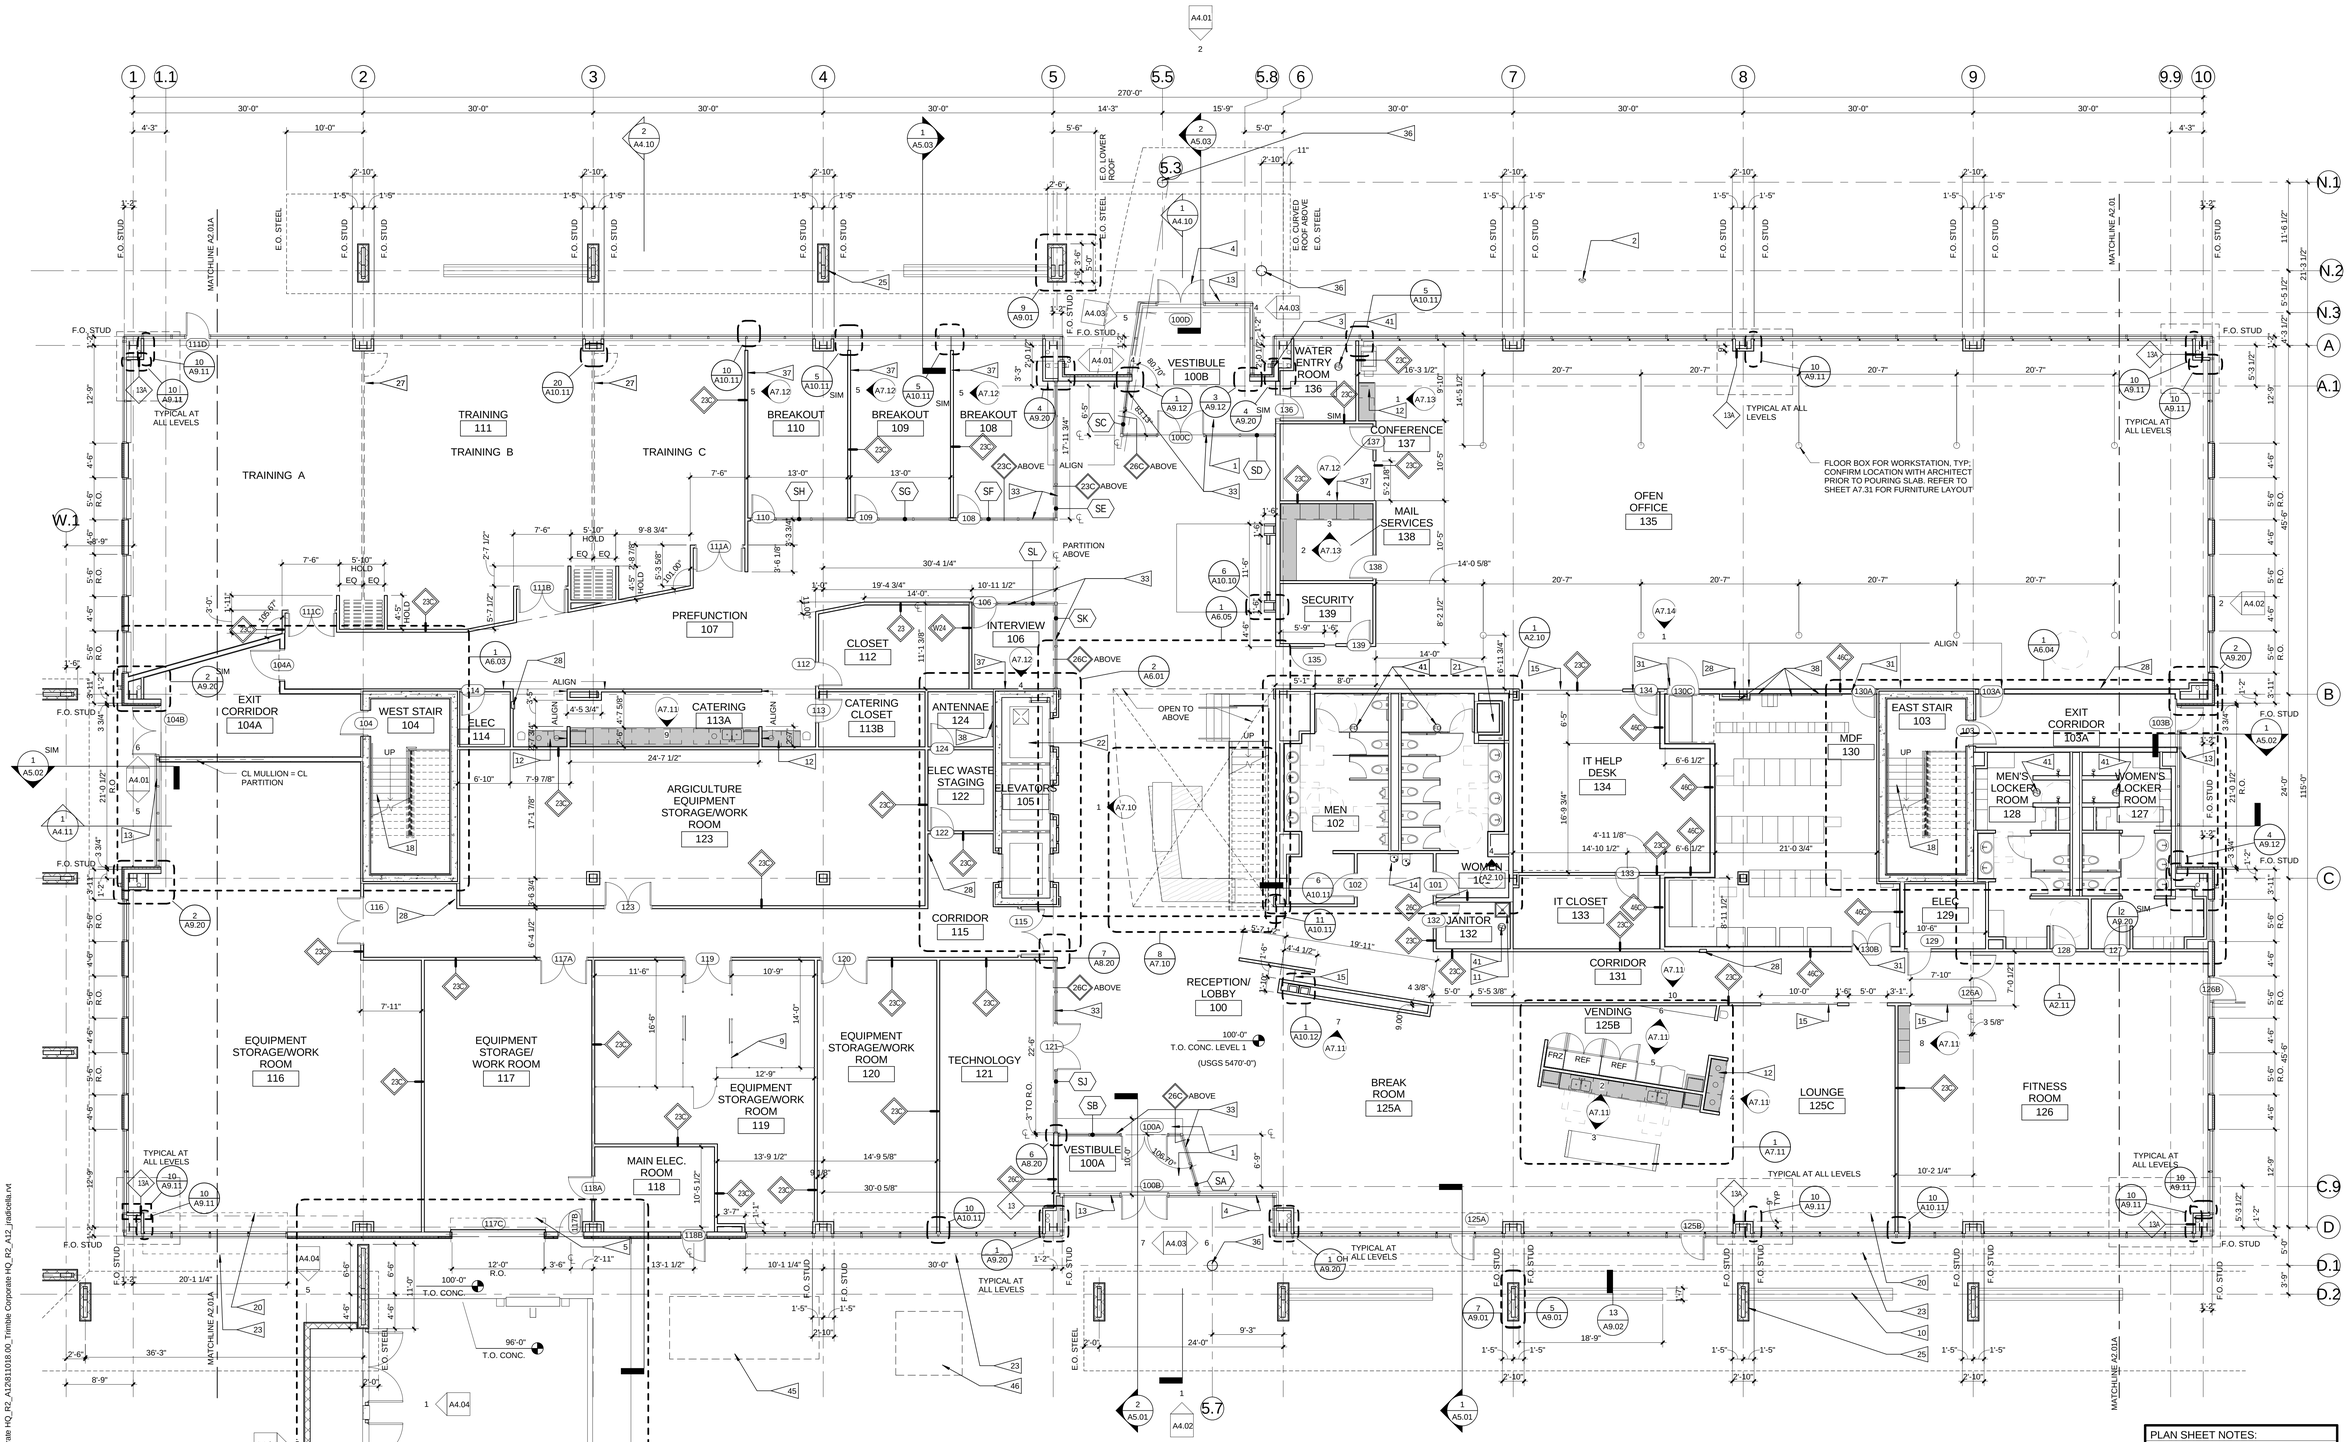


1 LEVEL 1 FLOOR PLAN

1/8" = 1'-0"

0' 4' 8' 16' 32'

PLAN FLAGNOTES:

1. WALKOFF CARPET MAT, RE SPECIFICATIONS.
2. FREESTANDING VERTICAL FIRE DEPARTMENT CONNECTION
3. FIRE DEPARTMENT KEY BOX
4. CURTAINWALL WINDOW AND DOOR SYSTEM, RE: SPECS.
5. OVERHEAD COILING DOOR, RE: SPECS
6. LOADING DOCK BUMPER, RE: SPECS
7. LOADING DOCK LEVELER, RE: SPECS
8. TRUCK LOCK, RE: SPECS
9. CHAINLINK FENCE, 9'-0" TALL, RE: SPECS. VERIFY EXTENTS OF EXISTING.
10. WOOD BENCH, RE: 13/A9.02
11. MOP SINK WITH MOP HOLDER, RE: PLUMBING
12. RECYCLING CONTAINER
13. SIGNAGE: NO SMOKING; RE:
14. DRINKING FOUNTAIN, RE: PLUMBING
15. 1/2" TEMPERED LAMINATED, BUTT JOINT, FULL-HEIGHTGLAZING SYSTEM SET IN U-CHANNELS. SEE DETAILS 2-4/A10.11
16. 4 FOOT TALL X 8" DIA CONCRETE BOLLARD
17. 42" HEIGHT DECORATIVE GLASS GUARDRAIL
18. CONCRETE FILLED STEEL PAN STAIR, RE: STRUCT.
19. KAWALL SKYLIGHT, RE: SPECS
20. INTERIOR LIGHT SHELF/SHADING DEVICE, 2'-6" DEEP AT SOUTH ELEVATION ONLY.
21. DUCT CHASE, RE: MECHANICAL
22. ELEVATOR, TOTAL OF 3, SEE SPECIFICATIONS
23. HORIZONTAL EXTERIOR LIGHT SHELF/SHADING DEVICE, 2'-6 DEEP AT SOUTH ELEVATION ONLY
24. CANOPY ROOF BELOW WITH TPO ROOFING
25. CANOPY COLUMN: MORTAR SET THIN-CLAD RENAISSANCE UNITS OVER CMU WALL
26. SITE WALL; RE: LANDSCAPE AND CIVIL
27. MOVEABLE PARTITION WALL, RE: SPECS
28. FIRE EXSTINGUISHER CABINET; RE: SPECS SEE DETAIL 8/A10.13
29. ROOF DRAIN; RE: PLUMBING. CONNECTED TO STORM DRAIN; RE: CIVIL
30. STEEL GATE, PAINTED TO MATCH CANOPY FASCIA
31. THE PERIMETER OF DOORS AT MDF ROOM TO BE SEALED WITH SELF-ADHESIVE NEOPRENE SMOKE SEAL. DOOR PLUGS AT BOTTOM CORNERS OF DOOR.
32. NOT USED
33. STOREFRONT WINDOW AND DOOR SYSTEM AT INTERIOR, RE: SPECS34NOT USED
35. NOT USED
36. STEEL TUBE COLUMN; RE: STRUCTURAL
37. WHITE BOARD PAINT WITH 1/4" HALF ROUND ALUMINUM TRIM AND ALUMINUM RAIL AT BOTTOM; RE: TYPICAL ELEV
38. 4' WIDE X 8' HIGH PLYWOOD BACKBOARD; FIRE RATED
39. NOT USED
40. NOT USED
41. FLOOR DRAIN, RE: PLUMBING
42. NOT USED
43. GUTTER WITH OPEN END, RE: SPECS
44. VERTICAL FINS MOUNTED TO CURTAIN WALL MULLION, WEST ELEVATION ONLY, RE: 13/A9.10
45. GENERATOR, RE: ELECT
46. TRANSFORMER, RE: ELECT
47. WALL MOUNTED BIKE RACKS, TOTAL OF 5 WITH A CAPACITY FOR 6 BIKES EA. RE: SPECS
48. NOT USED
49. CLEARSTORY; RE: INTERIOR ELEVATIONS

PLAN SHEET NOTES:

1. SEE SHEET A10.02 FOR PARTITION TYPES.
2. SEE CODE SHEET T2.1 THROUGH T2.8 FOR EXTENT AND CONSTRUCTION OF FIRE RATED PARTITION TYPES AND FLOOR/CLG ASSEMBLIES.
3. EXTERIOR DIMENSIONS ARE TO THE EXTERIOR FACE OF METAL STUD U.O.N.
4. INTERIOR DIMENSIONS ARE TO FACE OF GYP BOARD U.N.O.
5. ALL INTERIOR PARTITIONS ARE TYPE 23D U.O.N.
6. SEE 1/A8.15 FOR INTERIOR STOREFRONT FRAMES INDICATED AS (SX)
7. SEE INTERIOR ELEVATIONS FOR INTERIOR GLAZING/WINDOWS.
8. ALL DOORS TO BE OFFSET FROM ADJACENT PARTITION BY 4" TYP. U.N.O.
9. MILLWORK IDENTIFIED BY SHADING.

OZ ARCHITECTURE
1805 29th Street
Suite 2054
Boulder, Colorado 80301
phone 303.449.8900

TRIMBLE WESTMINSTER BUILDING PROJECT

10368 WESTMOOR DRIVE
WESTMINSTER, CO 80021-2712

PROJ. NO. 811018.00
DRAWN: JR
CHECKED: HK
APPROVED: RP
DATE: 5/21/2012
REVISIONS

© OZ ARCHITECTURE

TRIMBLE WESTMINSTER BUILDING PROJECT
ISSUED FOR:
100% CONSTRUCTION DOCUMENTS

SHEET TITLE:
LEVEL 1 FLOOR PLAN

SCALE: As indicated
SHEET NUMBER
A2.01

C:\Revit Local Files\811018.00_Trimble Corporate HQ_R2_A12\811018.00_Trimble Corporate HQ_R2_A12_radkotla.rvt
5/17/2012 3:38:11 PM